



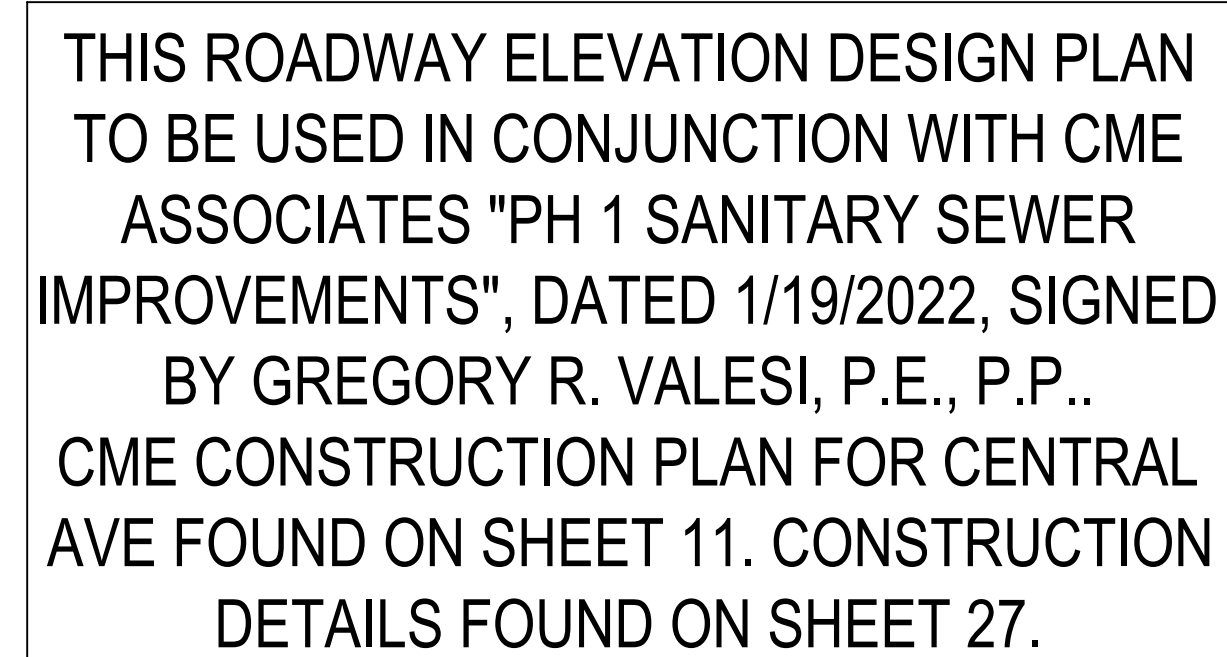

1. FIELD SURVEY PERFORMED AND PREPARED BY PS&S, SIGNED BY THOMAS J. MURPHY, DATED 04/19/2024.
2. ALL CURB DIMENSIONS SHOWN REFER TO THE FACE OF CURB.
3. CONSTANT SLOPES ARE MAINTAINED FROM IDENTIFIED HIGH POINTS TO LOW POINTS (INLETS OR OTHERWISE NOTED LOW POINTS).
4. BACK OF SIDEWALK ELEVATION GENERALLY TO MATCH TOP OF CURB ELEVATION EXCEPT AT DEPRESSIONS.
5. TRANSITIONS TO EXISTING DRIVEWAYS AND WALKWAYS TO BE SMOOTH.
6. CONTRACTOR SHALL FIELD VERIFY ALL DIMENSIONS PRIOR TO CONSTRUCTION & NOTIFY ENGINEER OF ANY DISCREPANCIES.
7. CONTRACTORS SHALL MAKE EVERY EFFORT TO NOT TRAP WATER ON PRIVATE PROPERTIES.

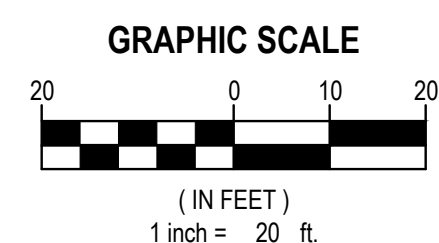

CONSULTANTS:		

MARK	DATE	DESCRIPTION

ALAN P. HILLA, JR., P.E.
NJ PROFESSIONAL ENGINEER LIC. NO. 24023284200
THIS SEAL MAY BE CONSIDERED AN OFFICIAL DOCUMENT AND IS TO REMAIN THE PROPERTY OF THE LICENSEE.

DESIGNED BY: CFH	DRAWN BY: CFH	CHECKED BY: CHW	REVIEWED BY: APH
PROJECT NO.: HLND 2303	DATE: MAY 2024	SCALE: AS SHOWN	

BOROUGH OF
HIGHLANDS

Phase 1 Sanitary
Sewer Improvements

Roadway Construction

STATUS


FOR CONSTRUCTION

SHEET TITLE


BEACH BOULEVARD ROADWAY
ELEVATION DESIGN PLAN

DRAWING No.

C 101.00

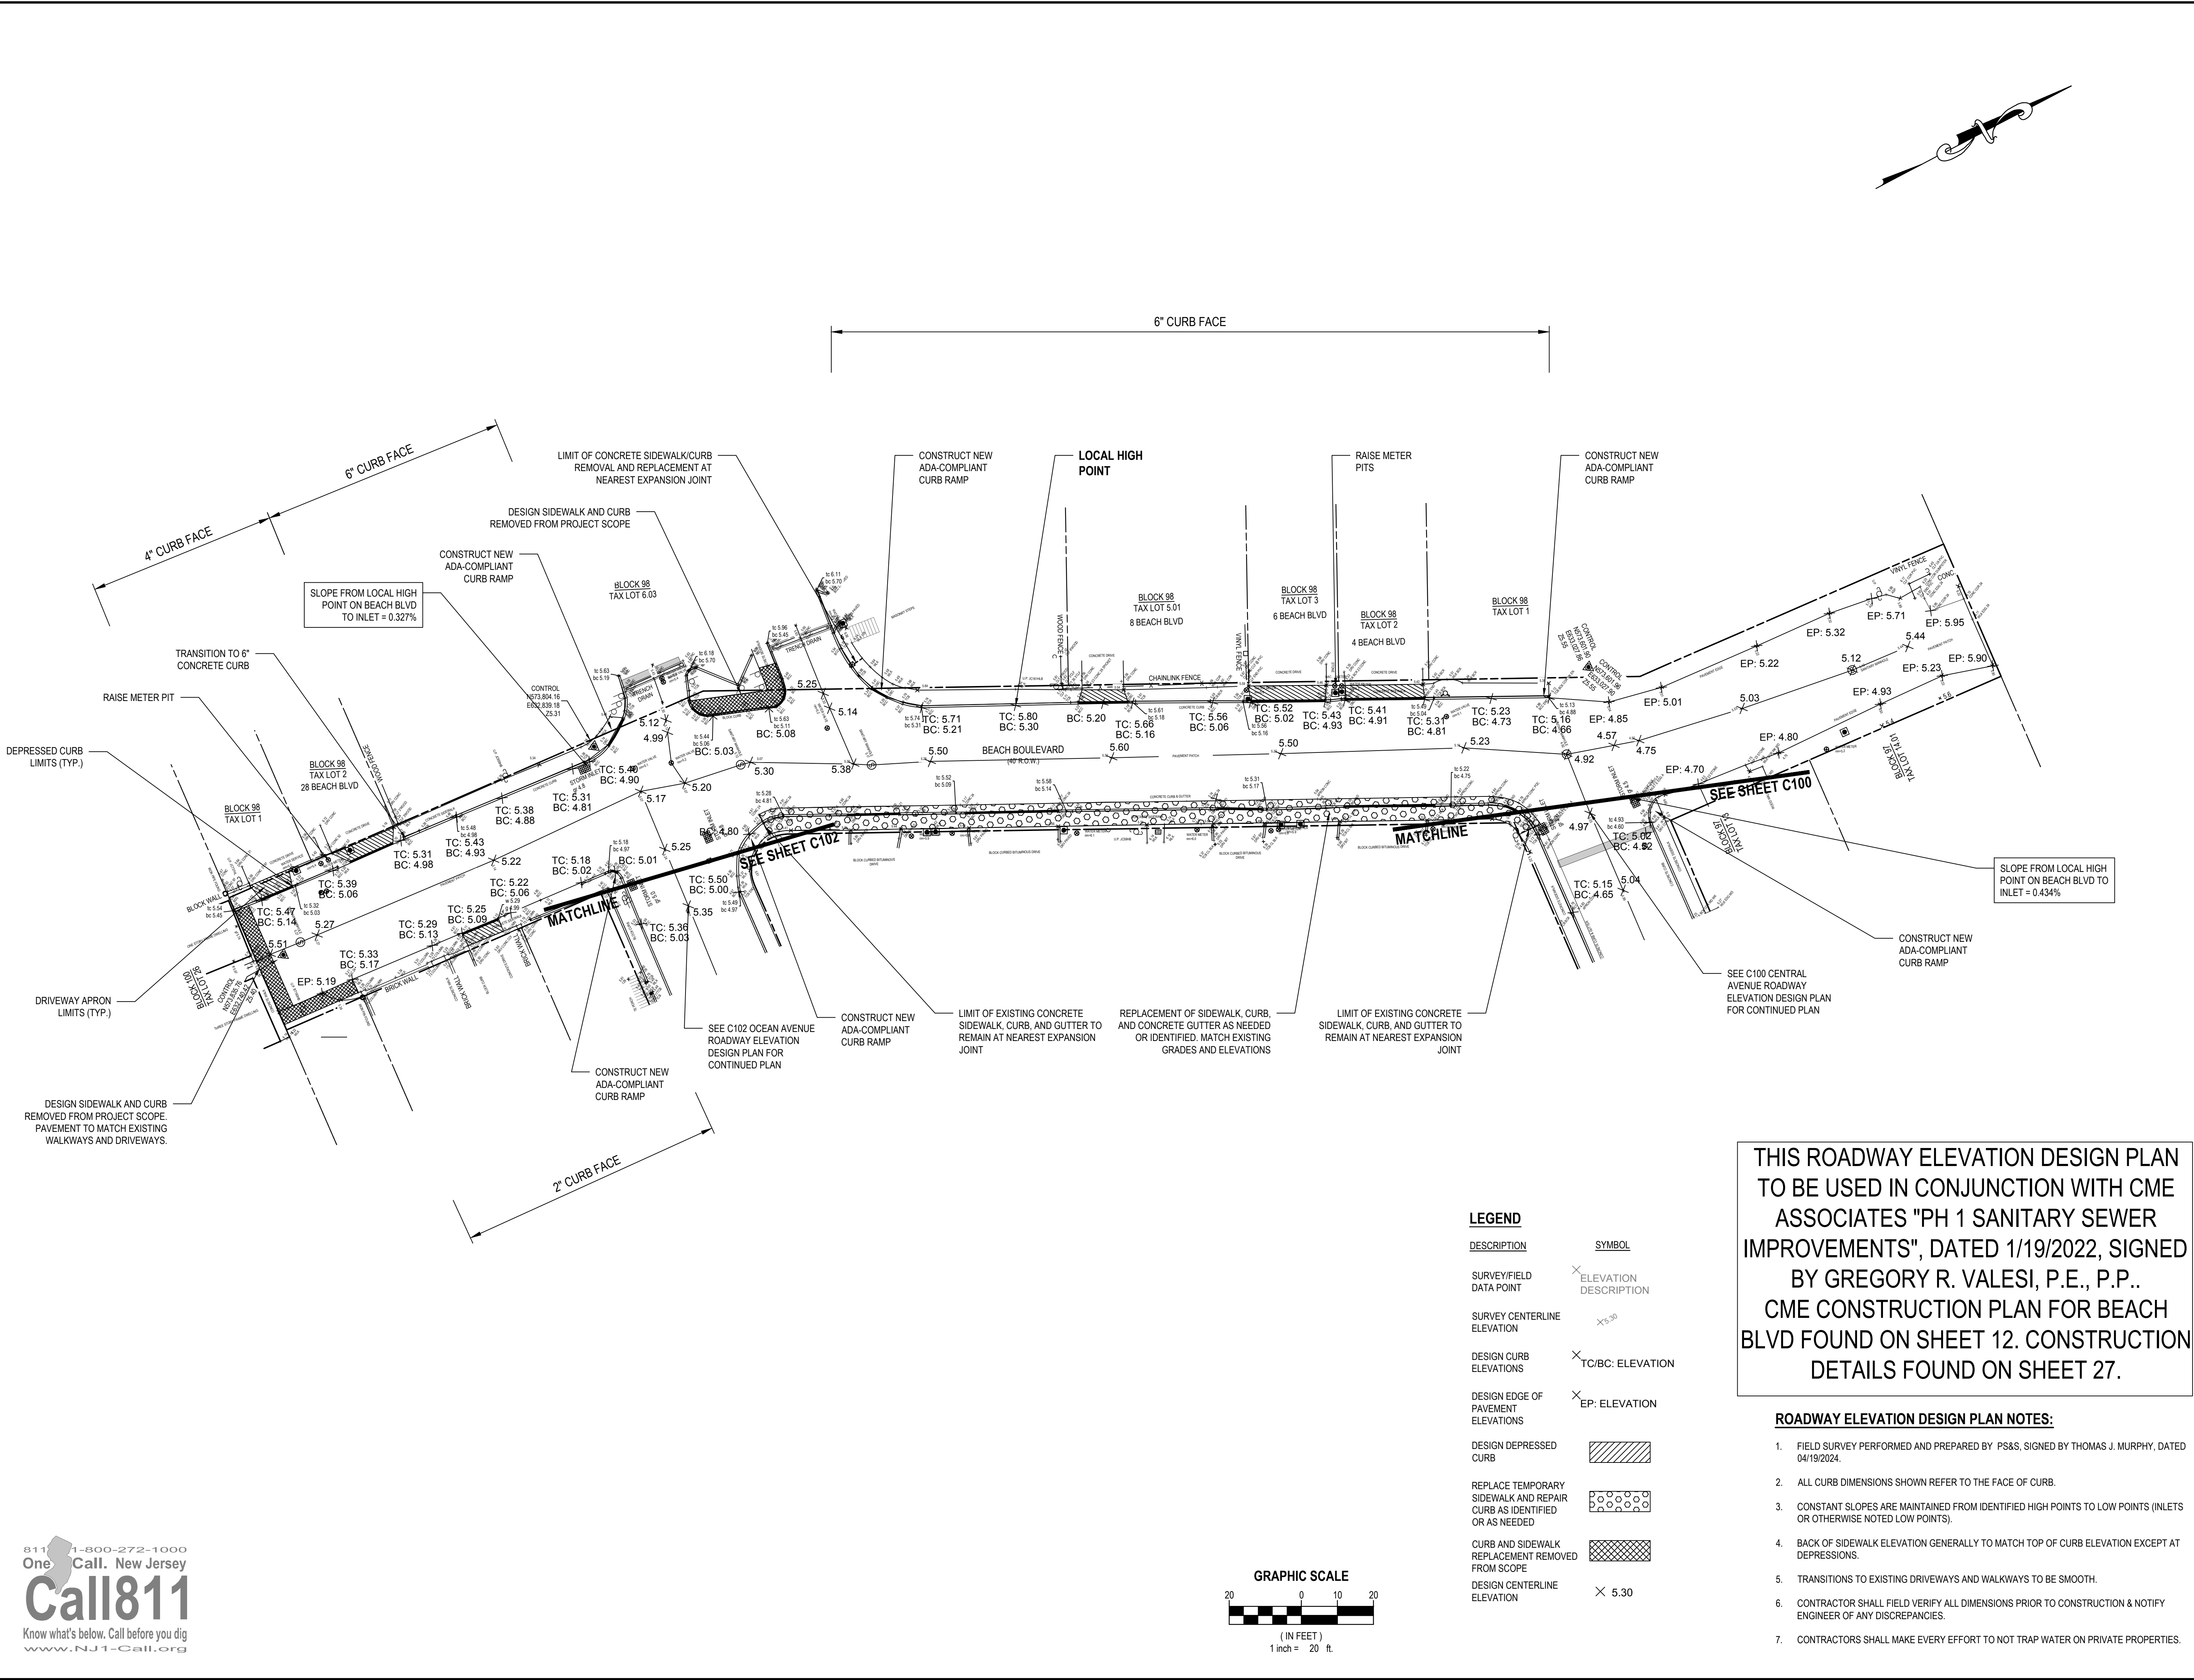

DESCRIPTION	SYMBOL
SURVEY/FIELD DATA POINT	✕ ELEVATION DESCRIPTION
SURVEY CENTERLINE ELEVATION	✕ 5.30
DESIGN CURB ELEVATIONS	✕ TC/BC: ELEVATION
DESIGN EDGE OF PAVEMENT ELEVATIONS	✕ EP: ELEVATION
DESIGN DEPRESSED CURB	
REPLACE TEMPORARY SIDEWALK AND REPAIR CURB AS IDENTIFIED OR AS NEEDED	
CURB AND SIDEWALK REPLACEMENT REMOVED FROM SCOPE	
DESIGN CENTERLINE ELEVATION	✕ 5.30

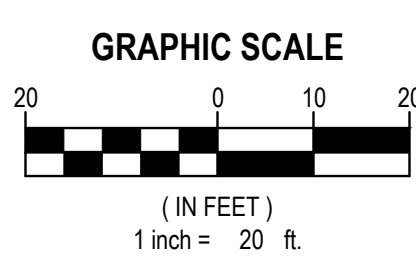

THIS ROADWAY ELEVATION DESIGN PLAN TO BE USED IN CONJUNCTION WITH CME ASSOCIATES "PH 1 SANITARY SEWER IMPROVEMENTS", DATED 1/19/2022, SIGNED BY GREGORY R. VALES, P.E., P.P.. CME CONSTRUCTION PLAN FOR BEACH BLVD FOUND ON SHEET 12. CONSTRUCTION DETAILS FOUND ON SHEET 27.

- ROADWAY ELEVATION DESIGN PLAN NOTES:
- FIELD SURVEY PERFORMED AND PREPARED BY: PS&S, SIGNED BY THOMAS J. MURPHY, DATED 04/19/2024.
 - ALL CURB DIMENSIONS SHOWN REFER TO THE FACE OF CURB.
 - CONSTANT SLOPES ARE MAINTAINED FROM IDENTIFIED HIGH POINTS TO LOW POINTS (INLETS OR OTHERWISE NOTED LOW POINTS).
 - BACK OF SIDEWALK ELEVATION GENERALLY TO MATCH TOP OF CURB ELEVATION EXCEPT AT DEPRESSIONS.
 - TRANSITIONS TO EXISTING DRIVEWAYS AND WALKWAYS TO BE SMOOTH.
 - CONTRACTOR SHALL FIELD VERIFY ALL DIMENSIONS PRIOR TO CONSTRUCTION & NOTIFY ENGINEER OF ANY DISCREPANCIES.
 - CONTRACTORS SHALL MAKE EVERY EFFORT TO NOT TRAP WATER ON PRIVATE PROPERTIES.

X:\LAND Highlands\HLND2303 - Phase 1 - Sanitary Improvements\02-BLM-CADD\Cor-Dwg\05-Curb-C 101 Beach Blvd Roadway Elevation Design Plan.dwg Last Modified: May 06, 2024 - 2:34pm By: jhilla

CONSULTANTS:		

MARK	DATE	DESCRIPTION

ALAN P. HILLA, JR., P.E.
NJ PROFESSIONAL ENGINEER L.C. NO. 2400280400
THIS SEAL MAY BE CONSIDERED AN OFFICIAL DOCUMENT AND IS TO BE KEPT IN THE POSSESSION OF THE LICENSEE.

DESIGNED BY: CFH	DRAWN BY: CFH	CHECKED BY: CHW	REVIEWED BY: APH
PROJECT NO.: HLND 2303	DATE: MAY 2024	SCALE: AS SHOWN	

BOROUGH OF
HIGHLANDS


Phase 1 Sanitary
Sewer Improvements

Roadway Construction

STATUS
FOR CONSTRUCTION

SHEET TITLE
OCEAN AVENUE ROADWAY
ELEVATION DESIGN PLAN

DRAWING No.
C 102.00

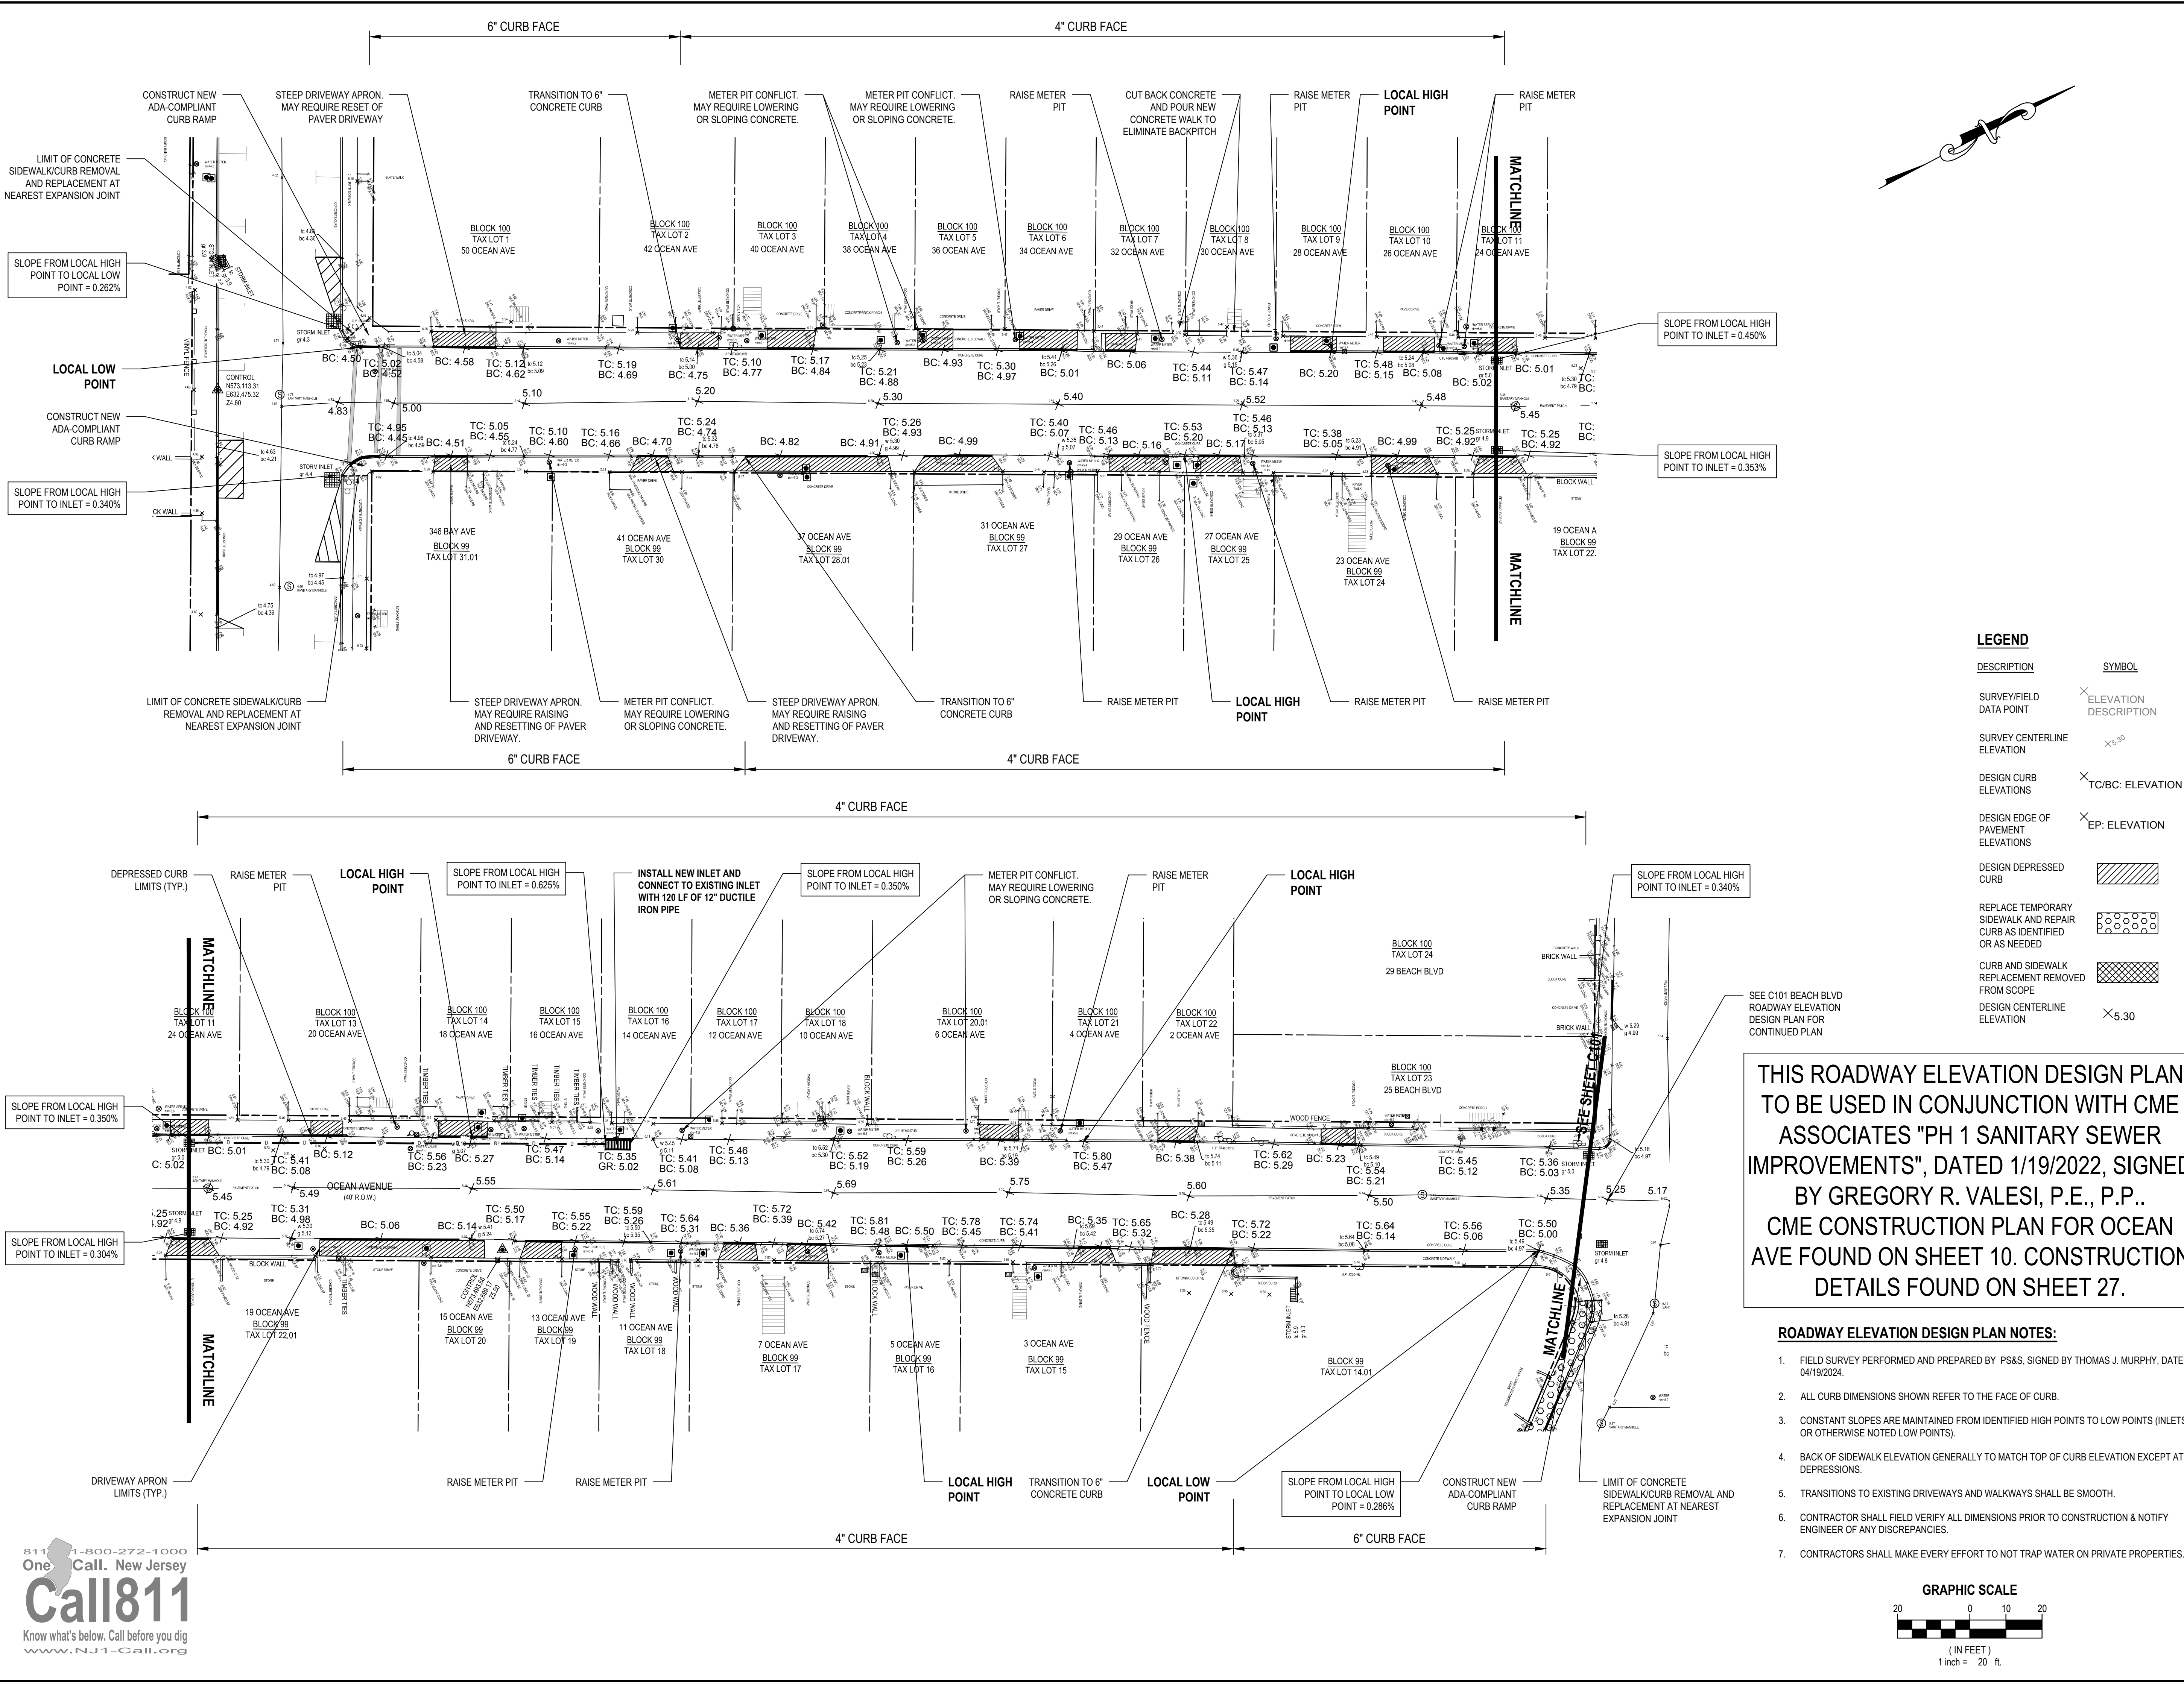

811 1-800-272-1000
One Call. New Jersey
Call811
Know what's below. Call before you dig
www.NJ1-Call.org